

INTERIOR
DESIGN

RESIDENTIAL
COMMERCIAL
HOSPITALITY
SPACE PLANNING
INTERIOR STYLING


PORTFOLIO

EEVON CHIEW NYU WEN


2026

SPACE
PEOPLE
LIFESTYLE
STORY


LAYOUT PLAN
- RESIDENTIAL -
(LANDED HOUSE PROJECT)

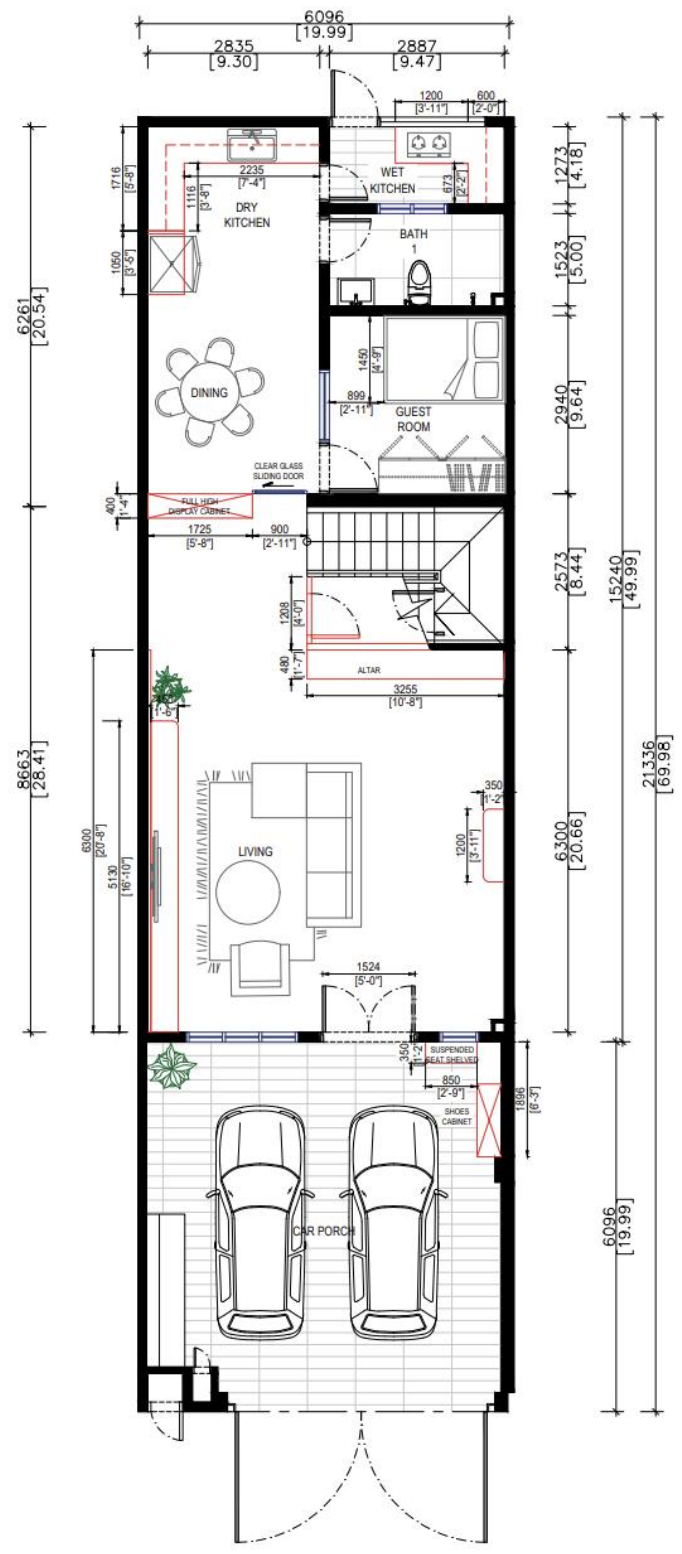

GROUND FLOOR PLAN
1:50

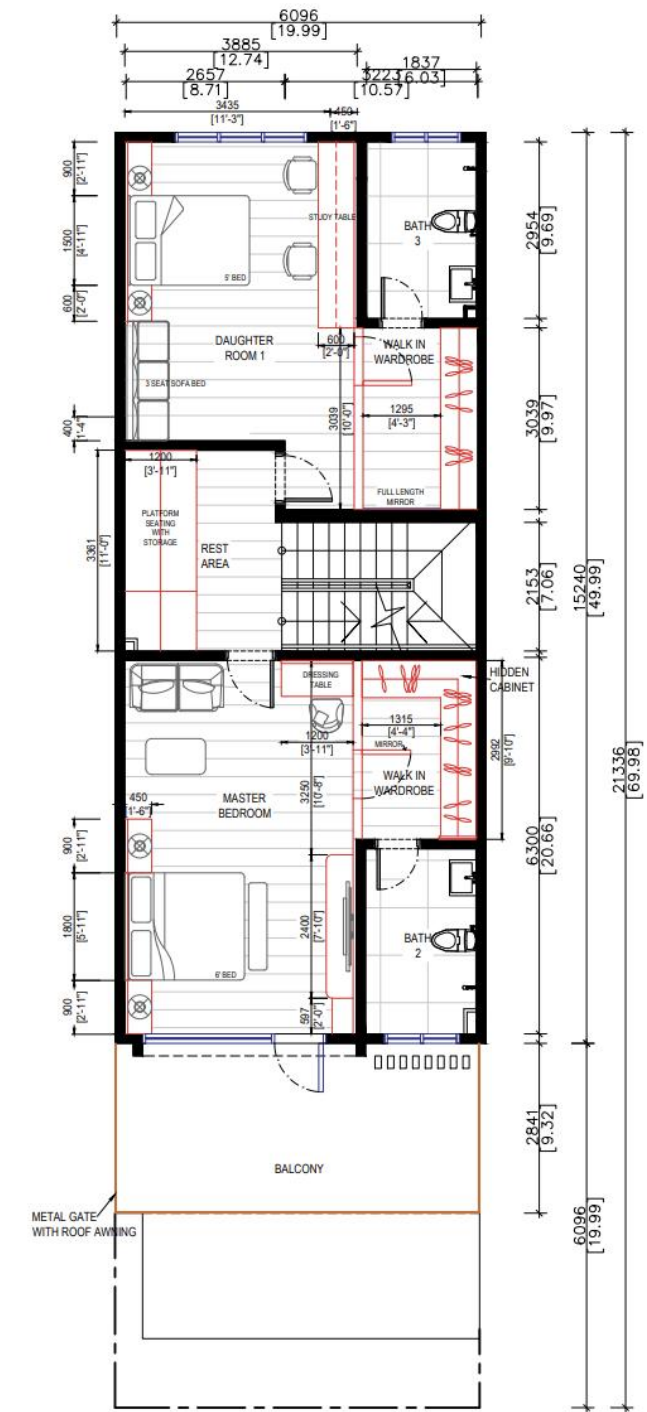


FIRST FLOOR PLAN
1:50

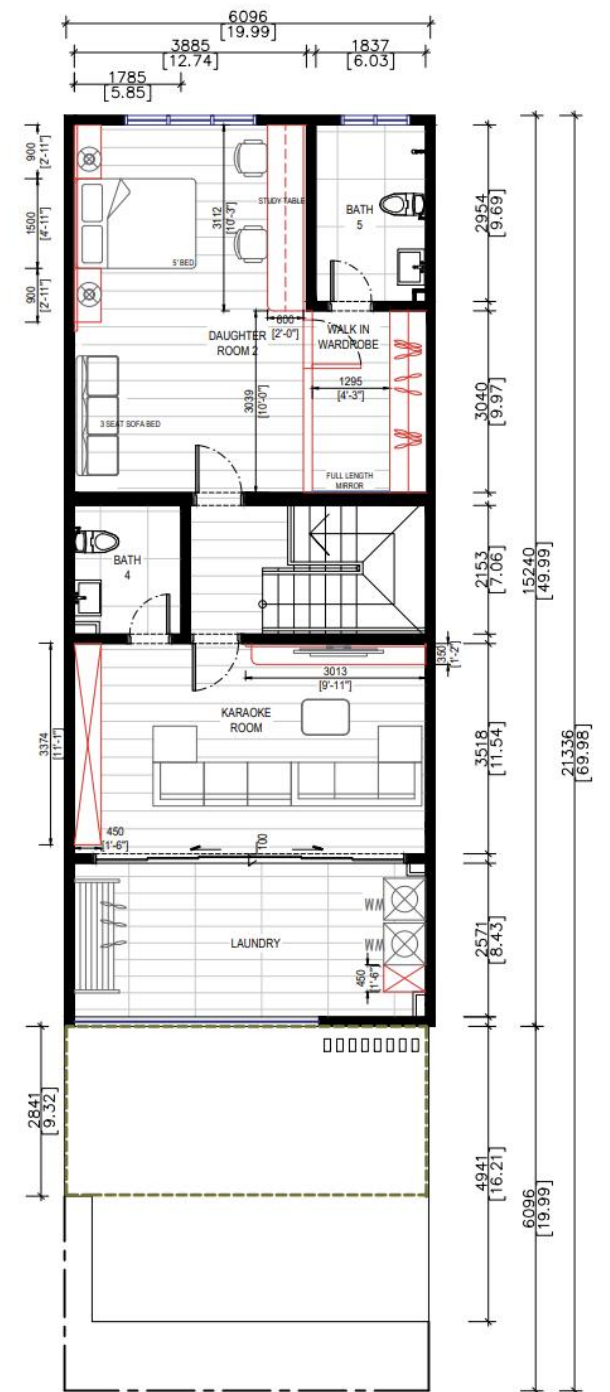

SECOND FLOOR PLAN
1:50

LAYOUT PLAN
- RESIDENTIAL -
(CONDO PROJECT)

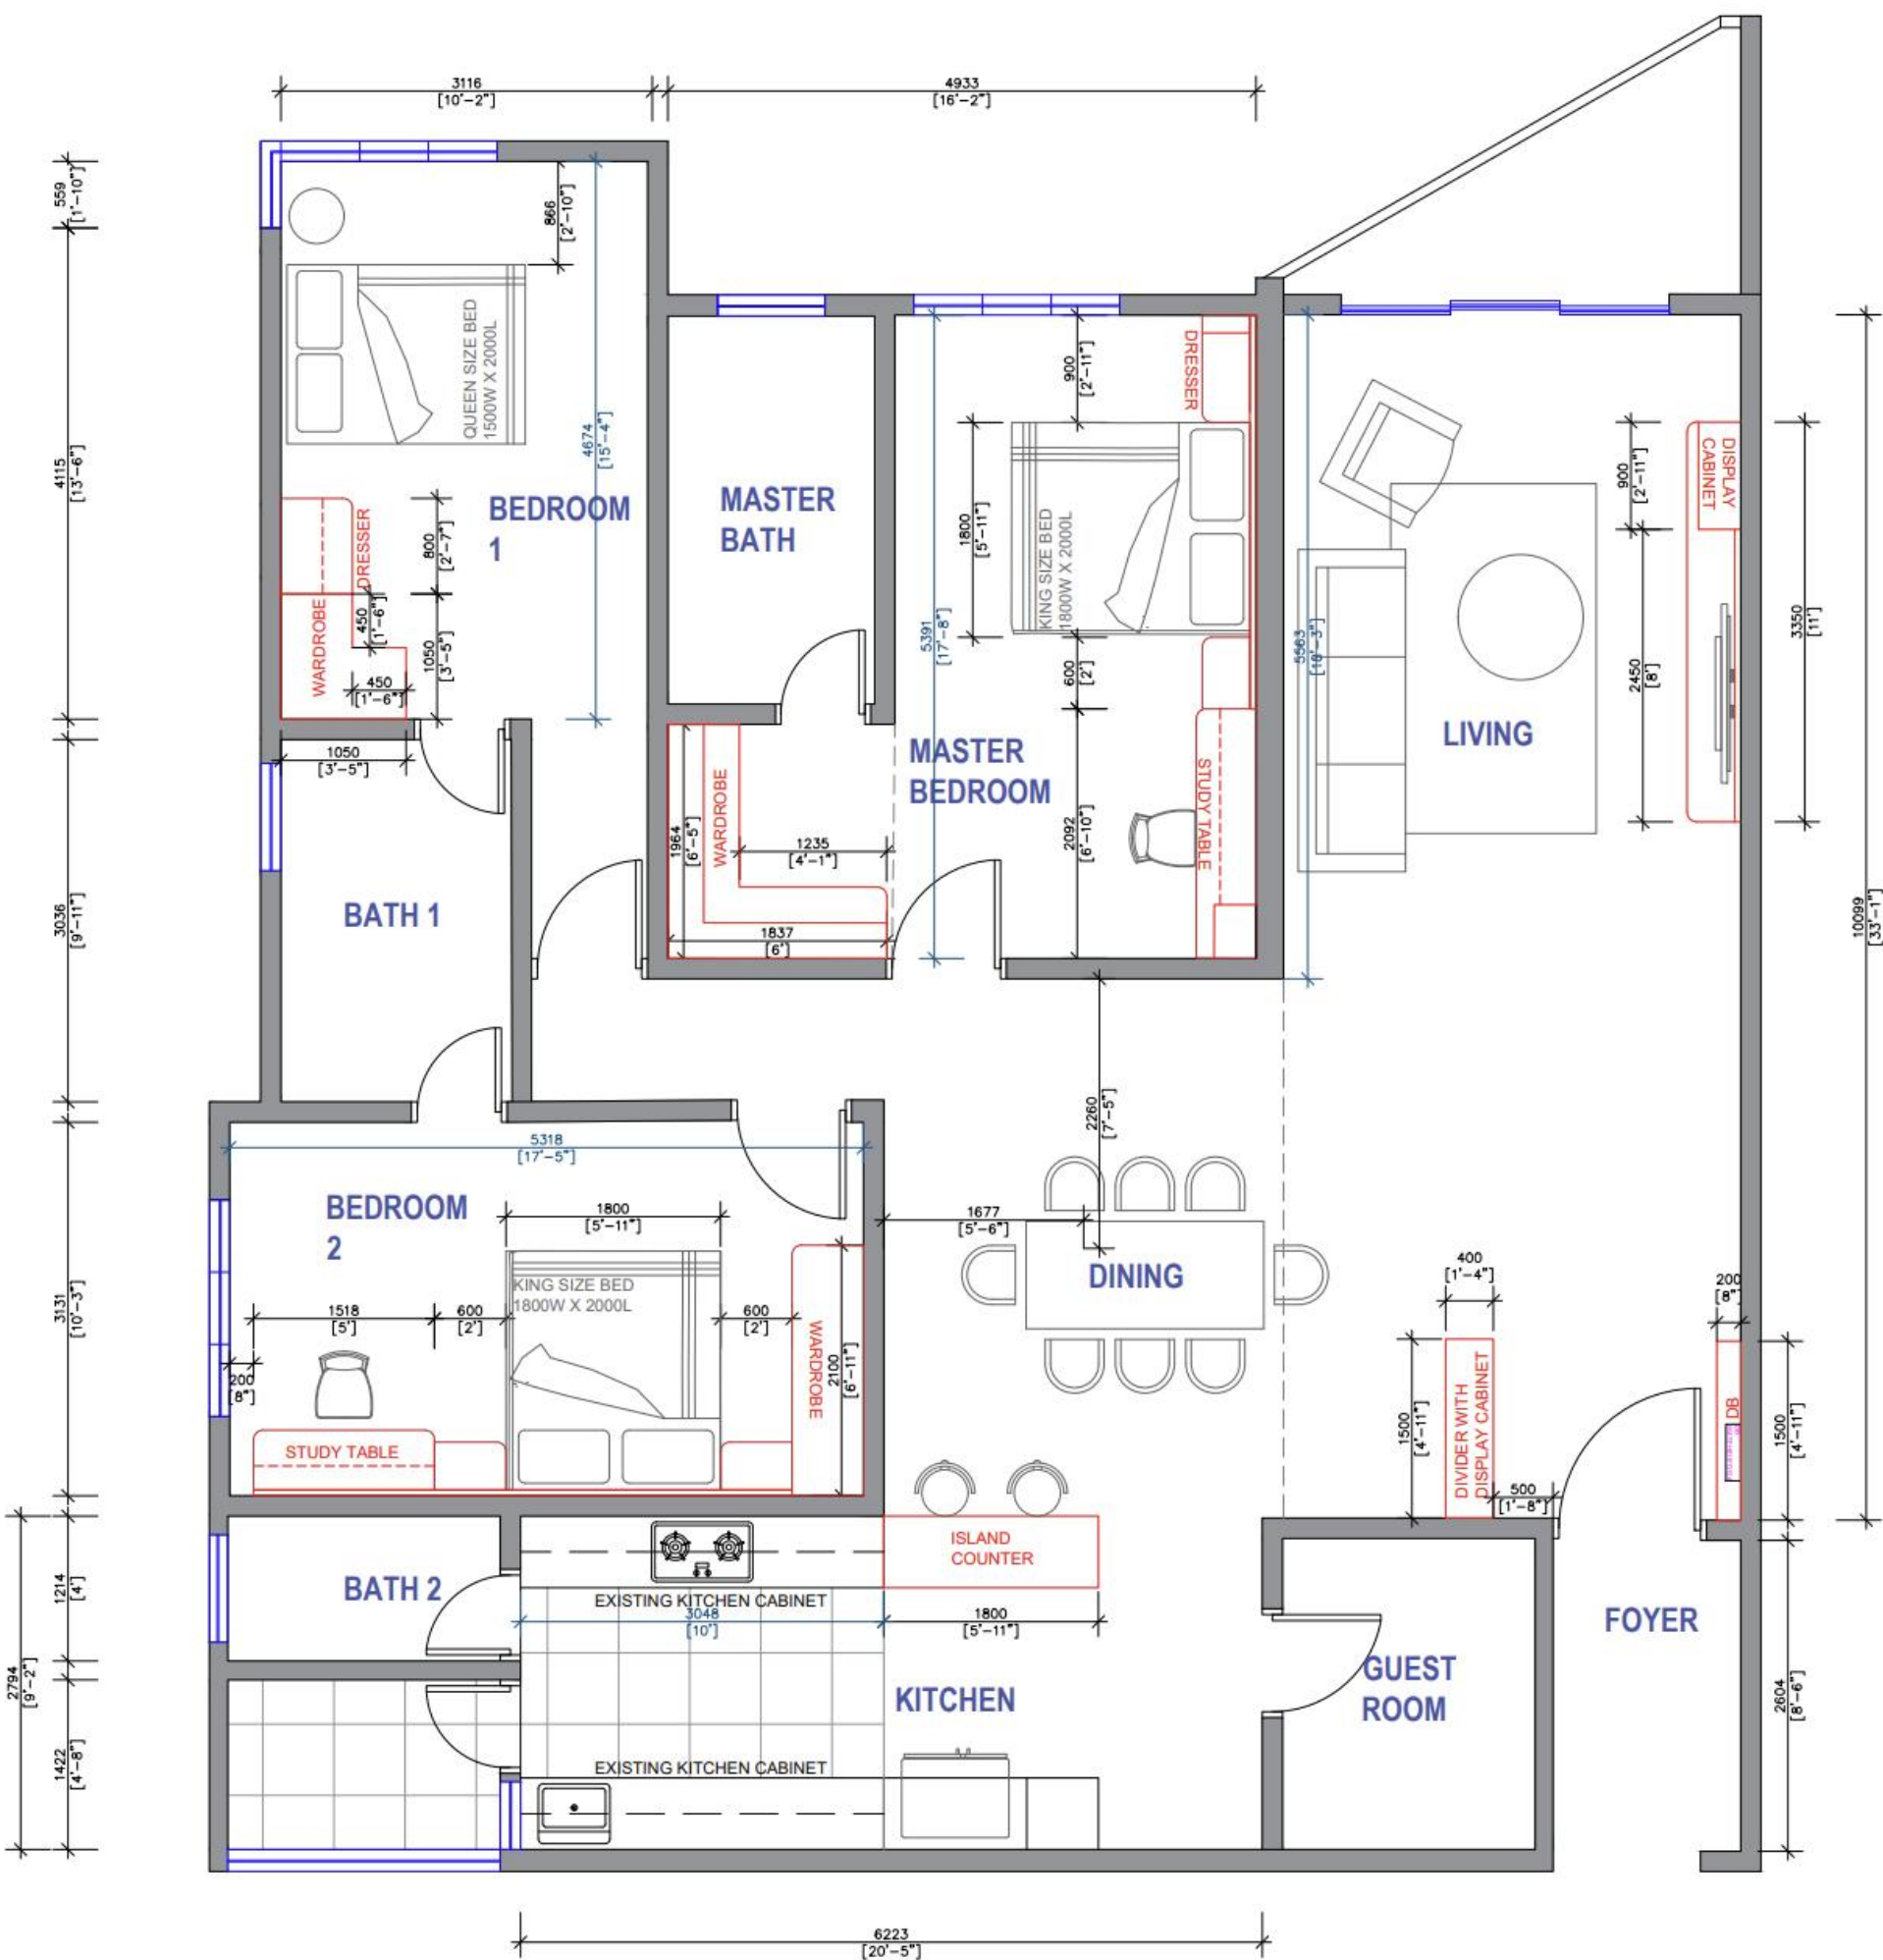



**NEW AWNING
(TEMPORARY OPEN AIR CONCEPT)**

NEW AWNING
(TEMPORARY OPEN AIR CONCEPT)


LAYOUT PLAN
- COMMERCIAL -
(OFFICE PROJECT)




M&E PLAN
- RESIDENTIAL -
(LANDED HOUSE PROJECT)

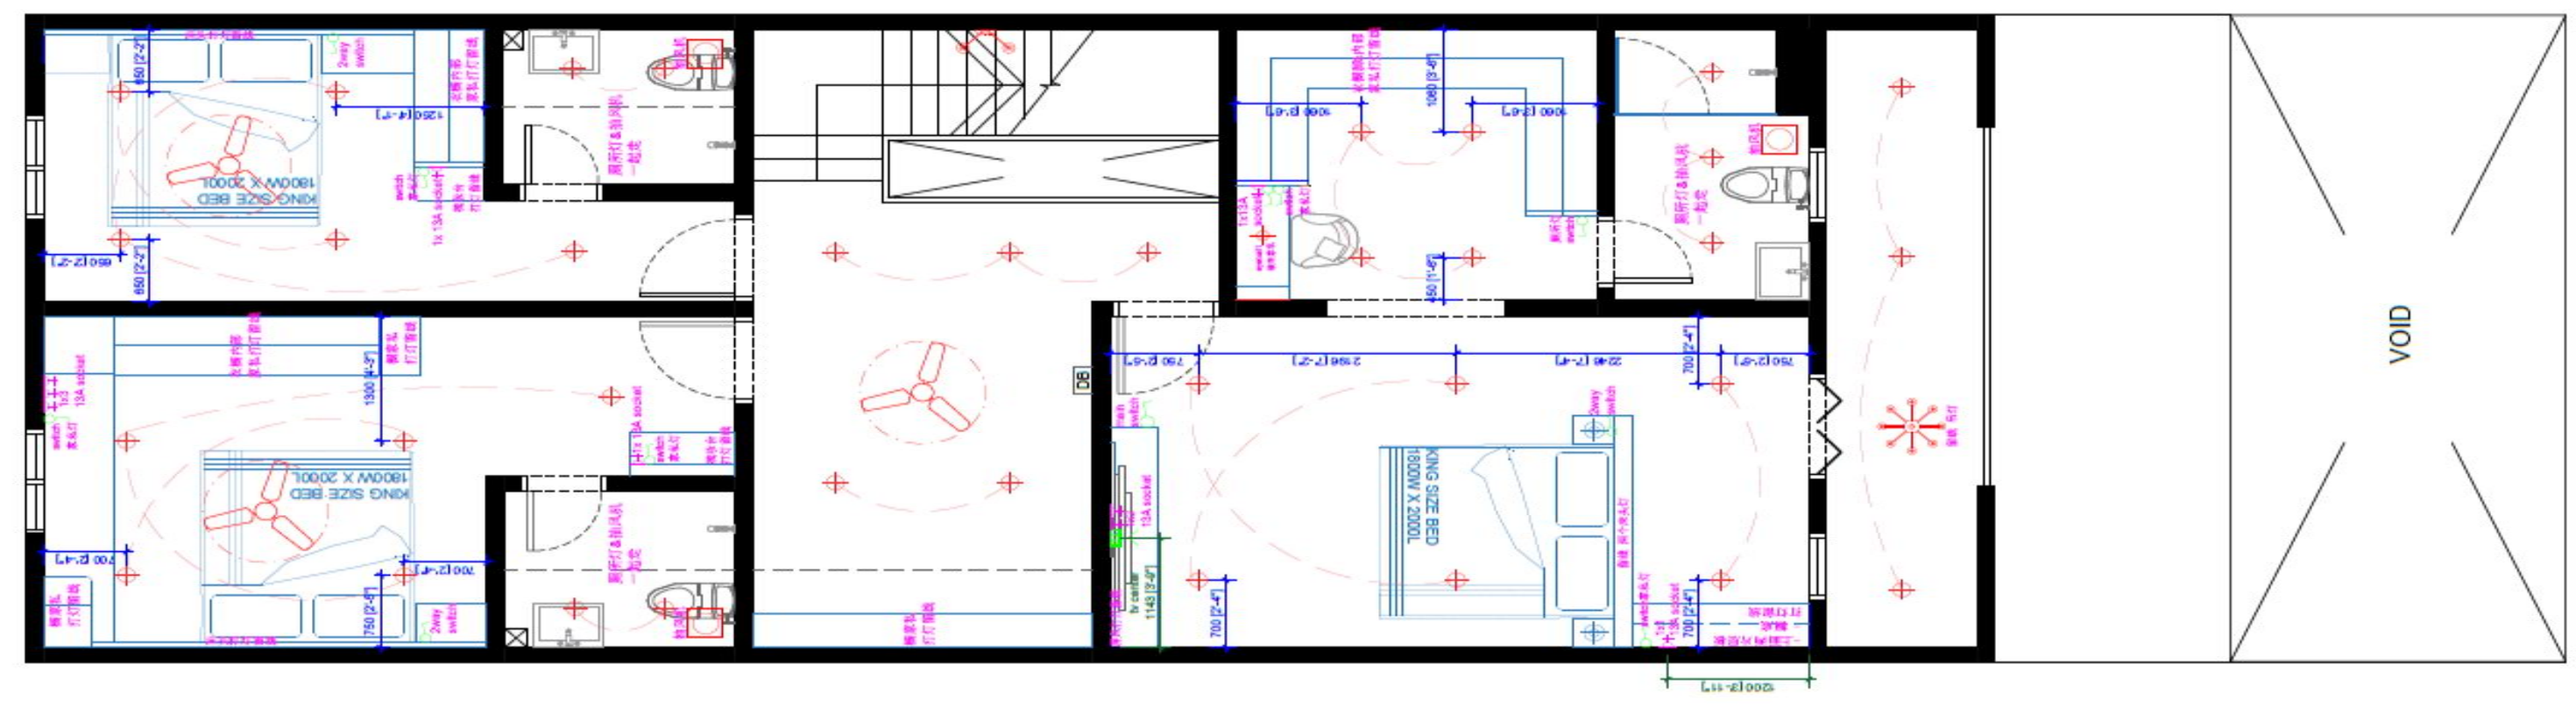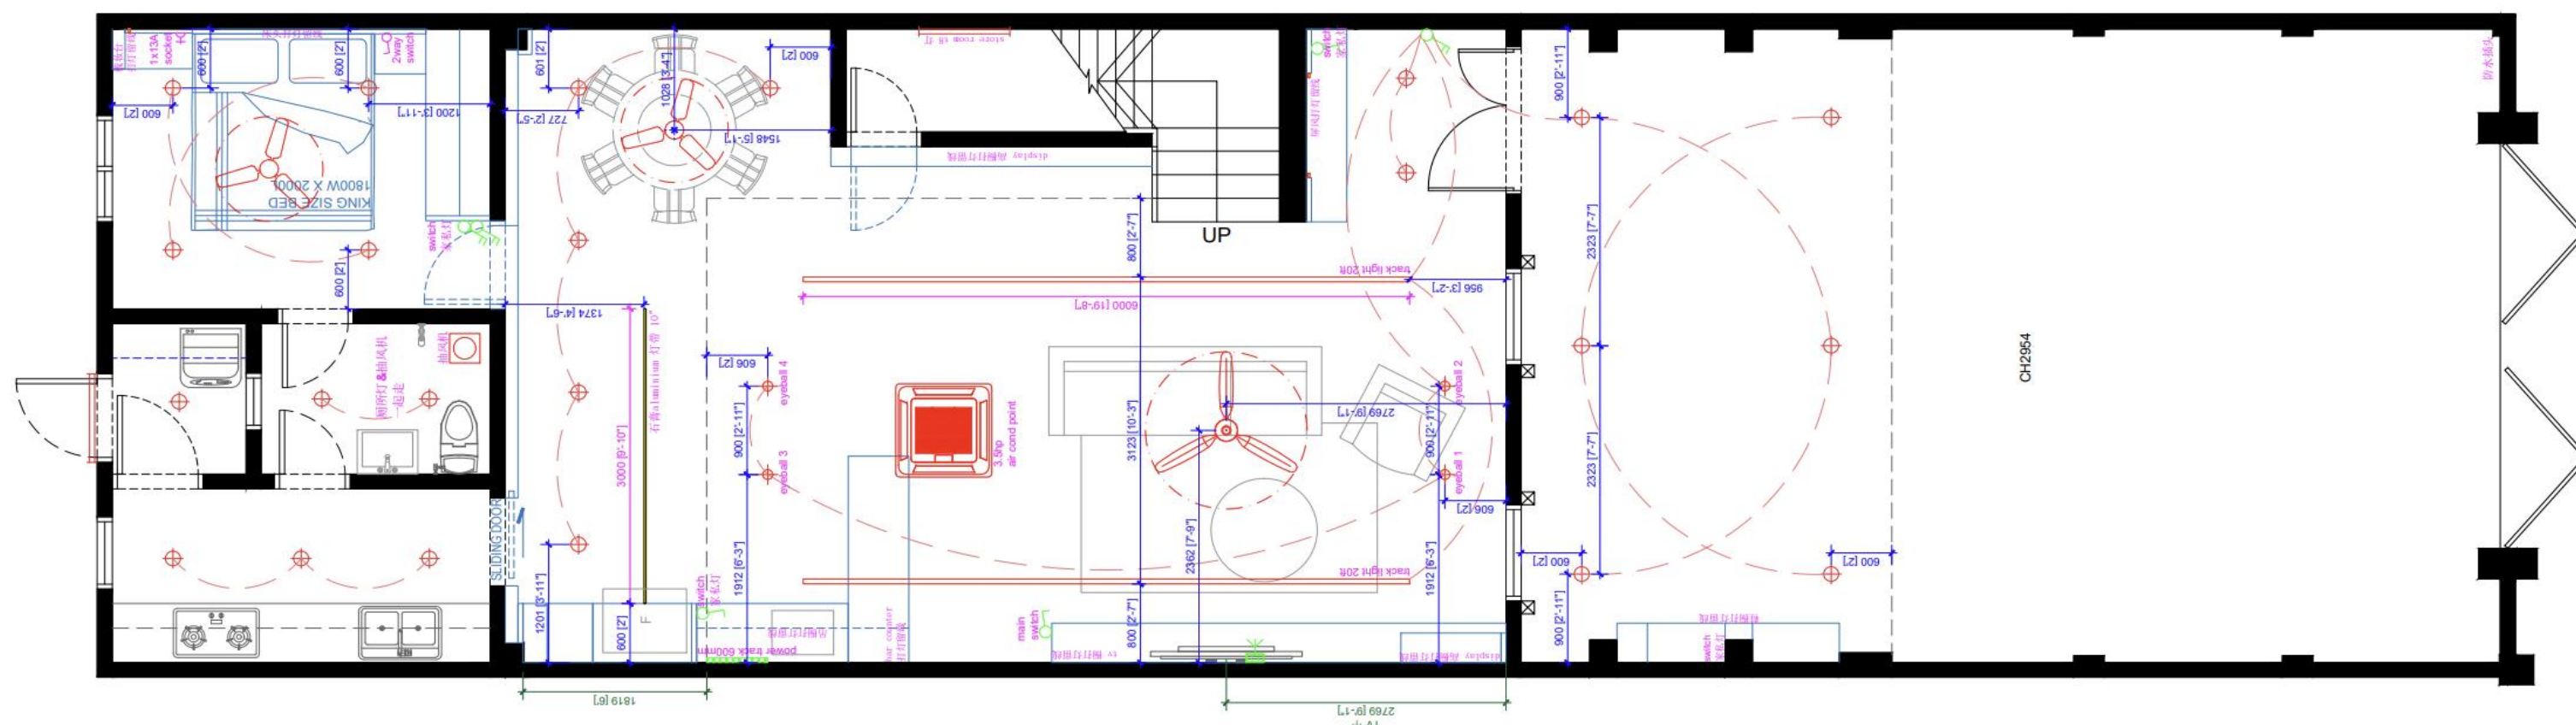

CARPENTRY DRAWING
- ELEVATION -
(KITCHEN AREA)



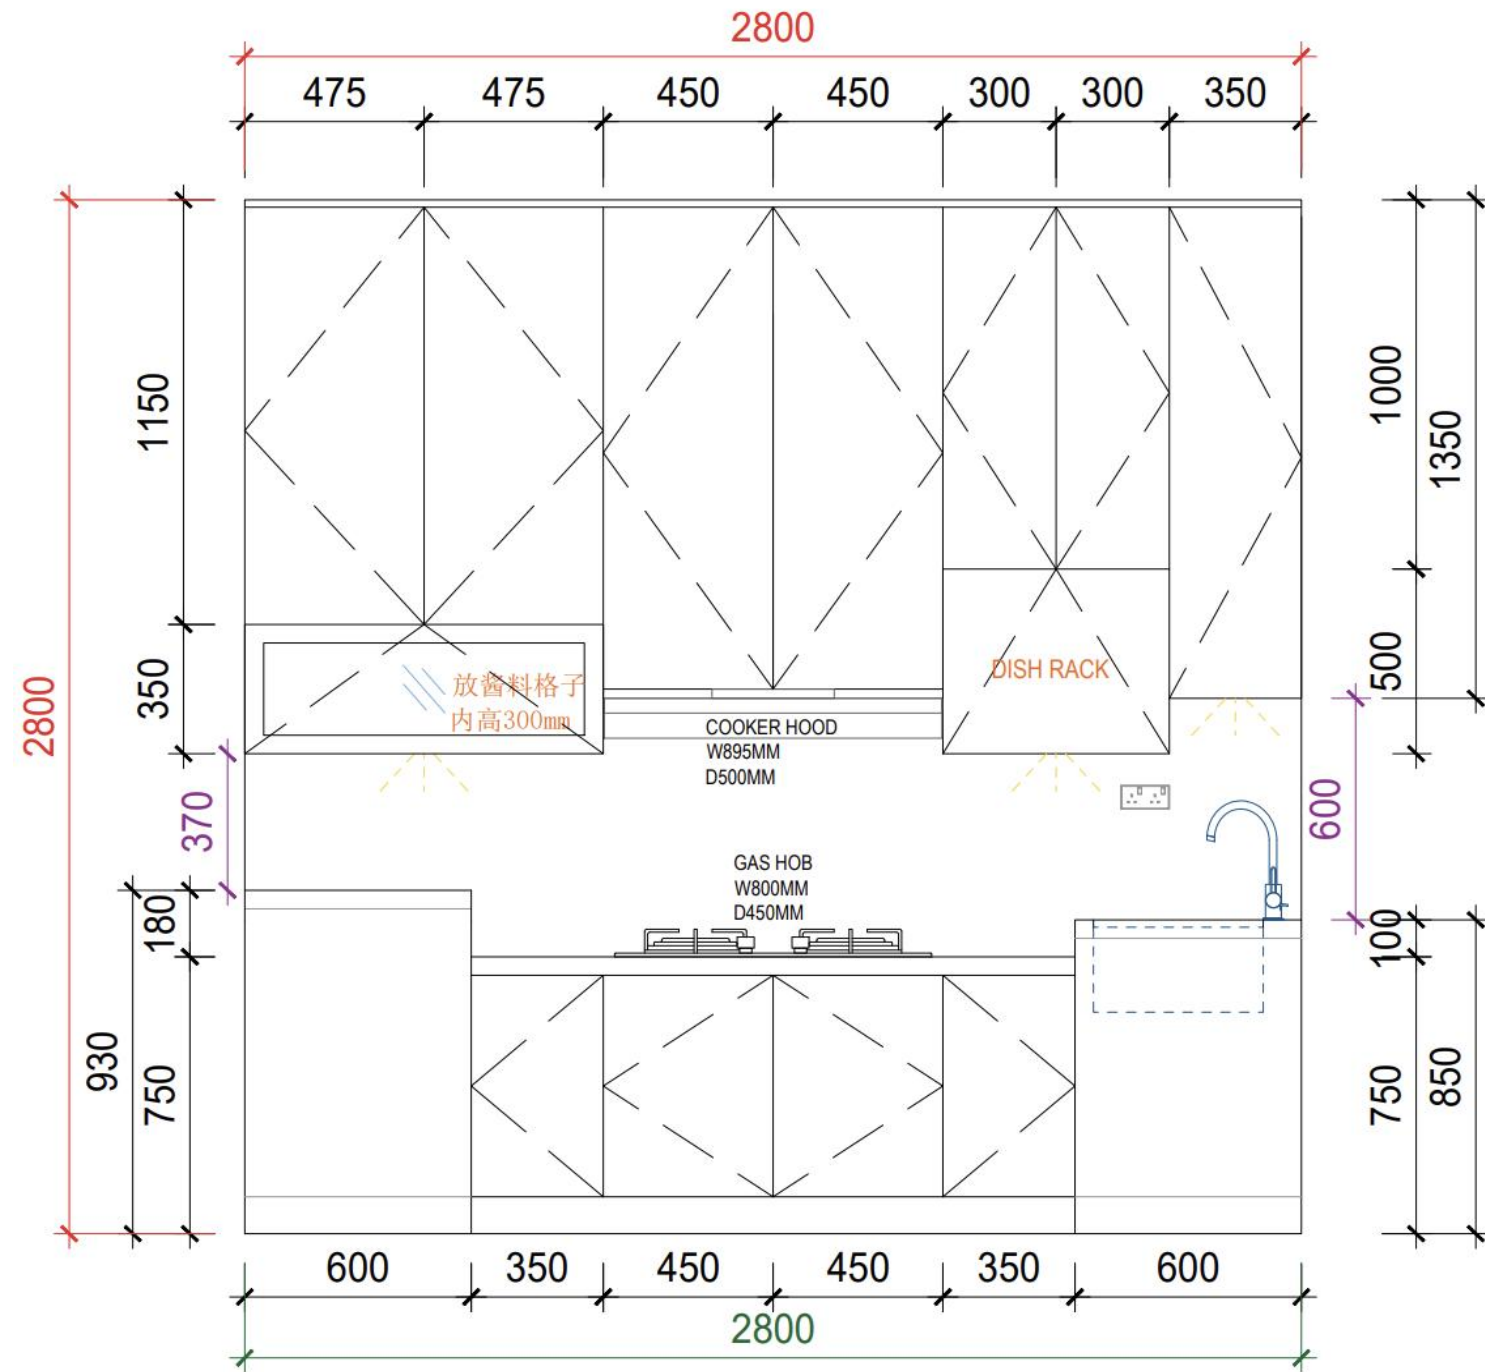


WET KITCHEN ELEVATION -B
1:10

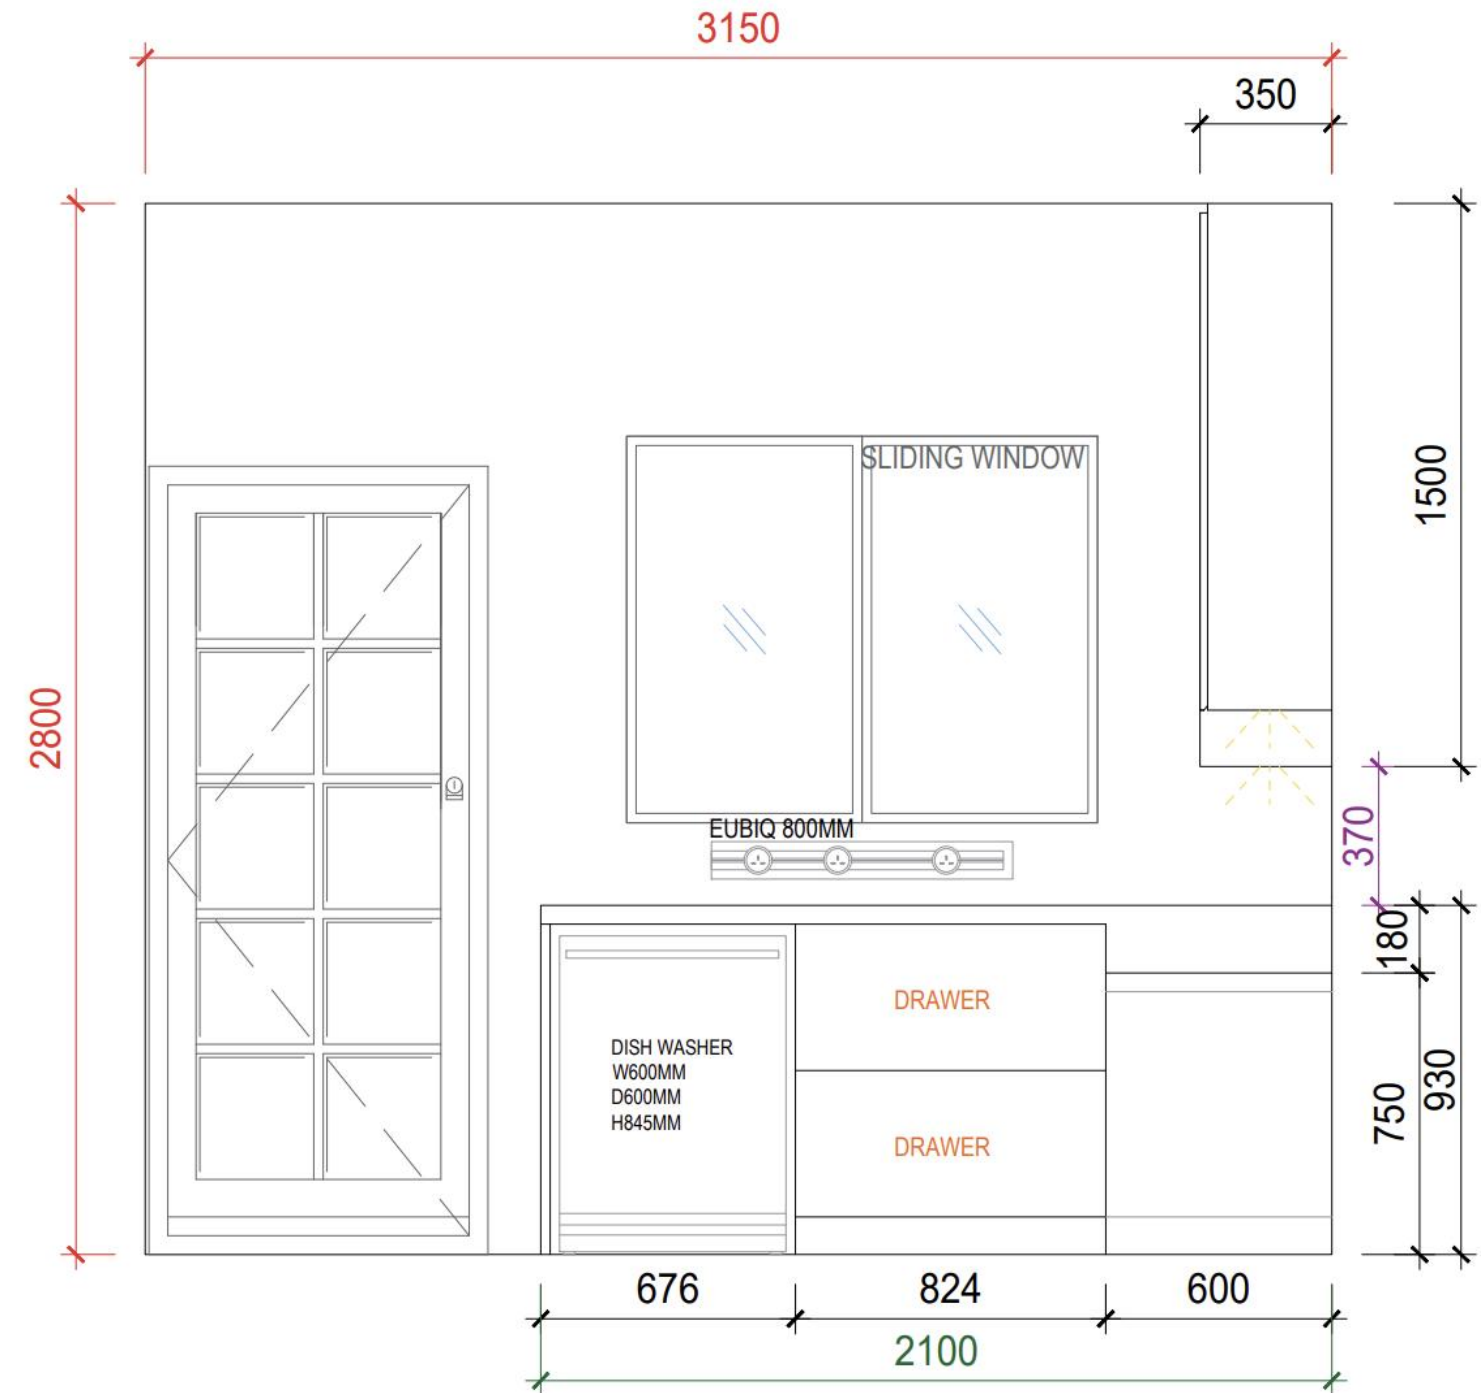


WET KITCHEN ELEVATION -A
1:10

CARPENTRY DRAWING
- ELEVATION -
(BEDROOM AREA)

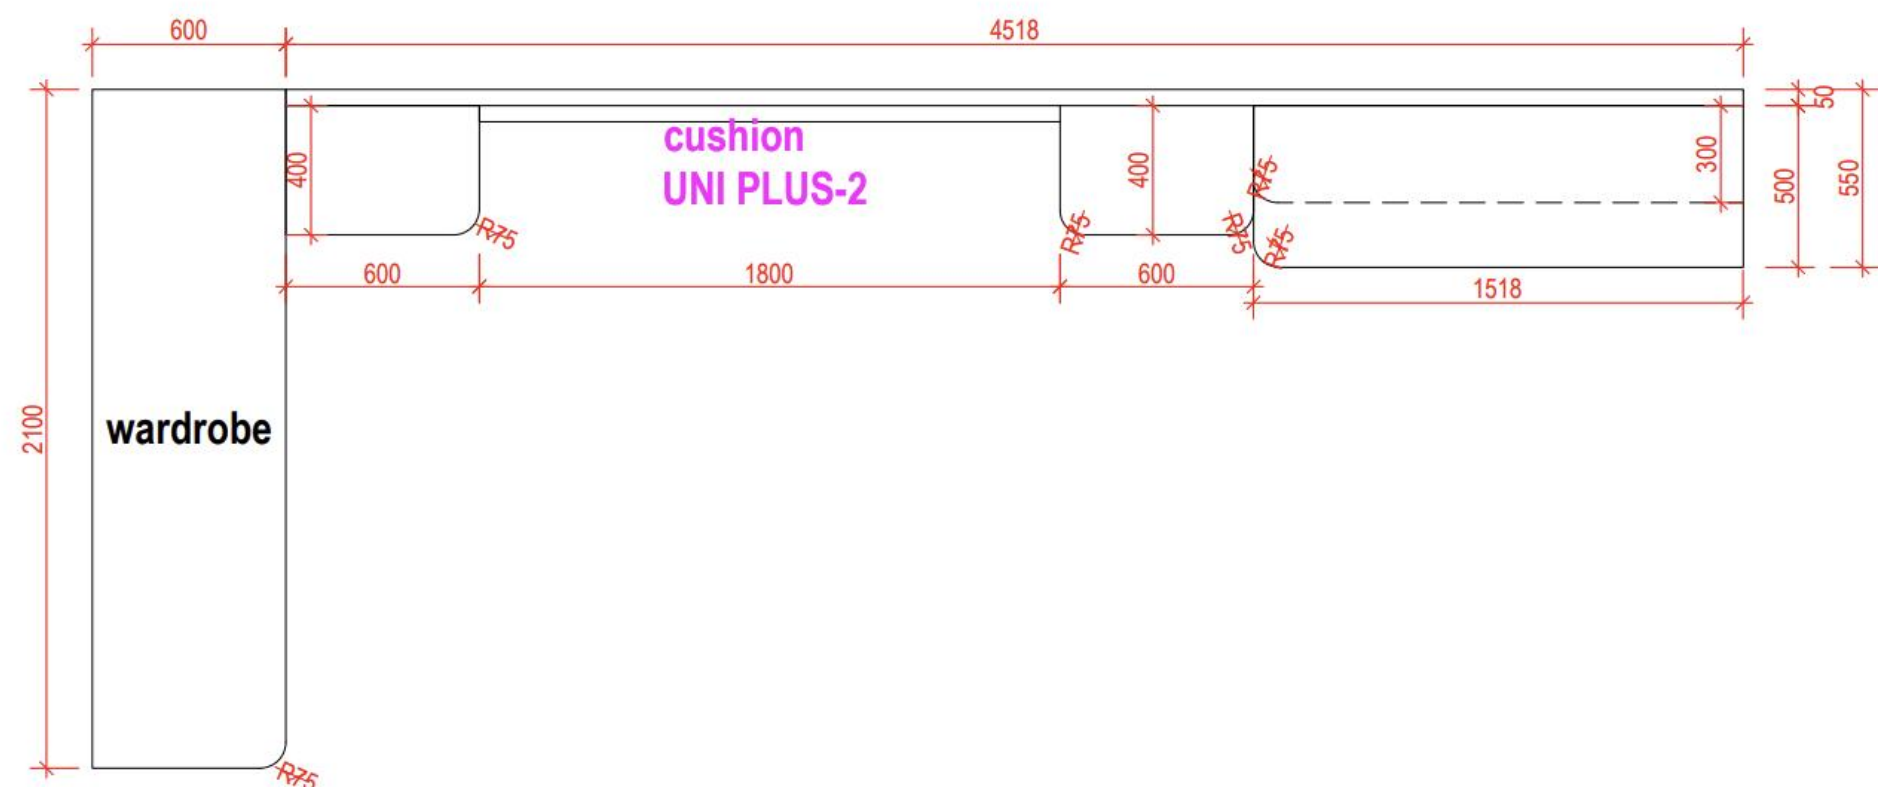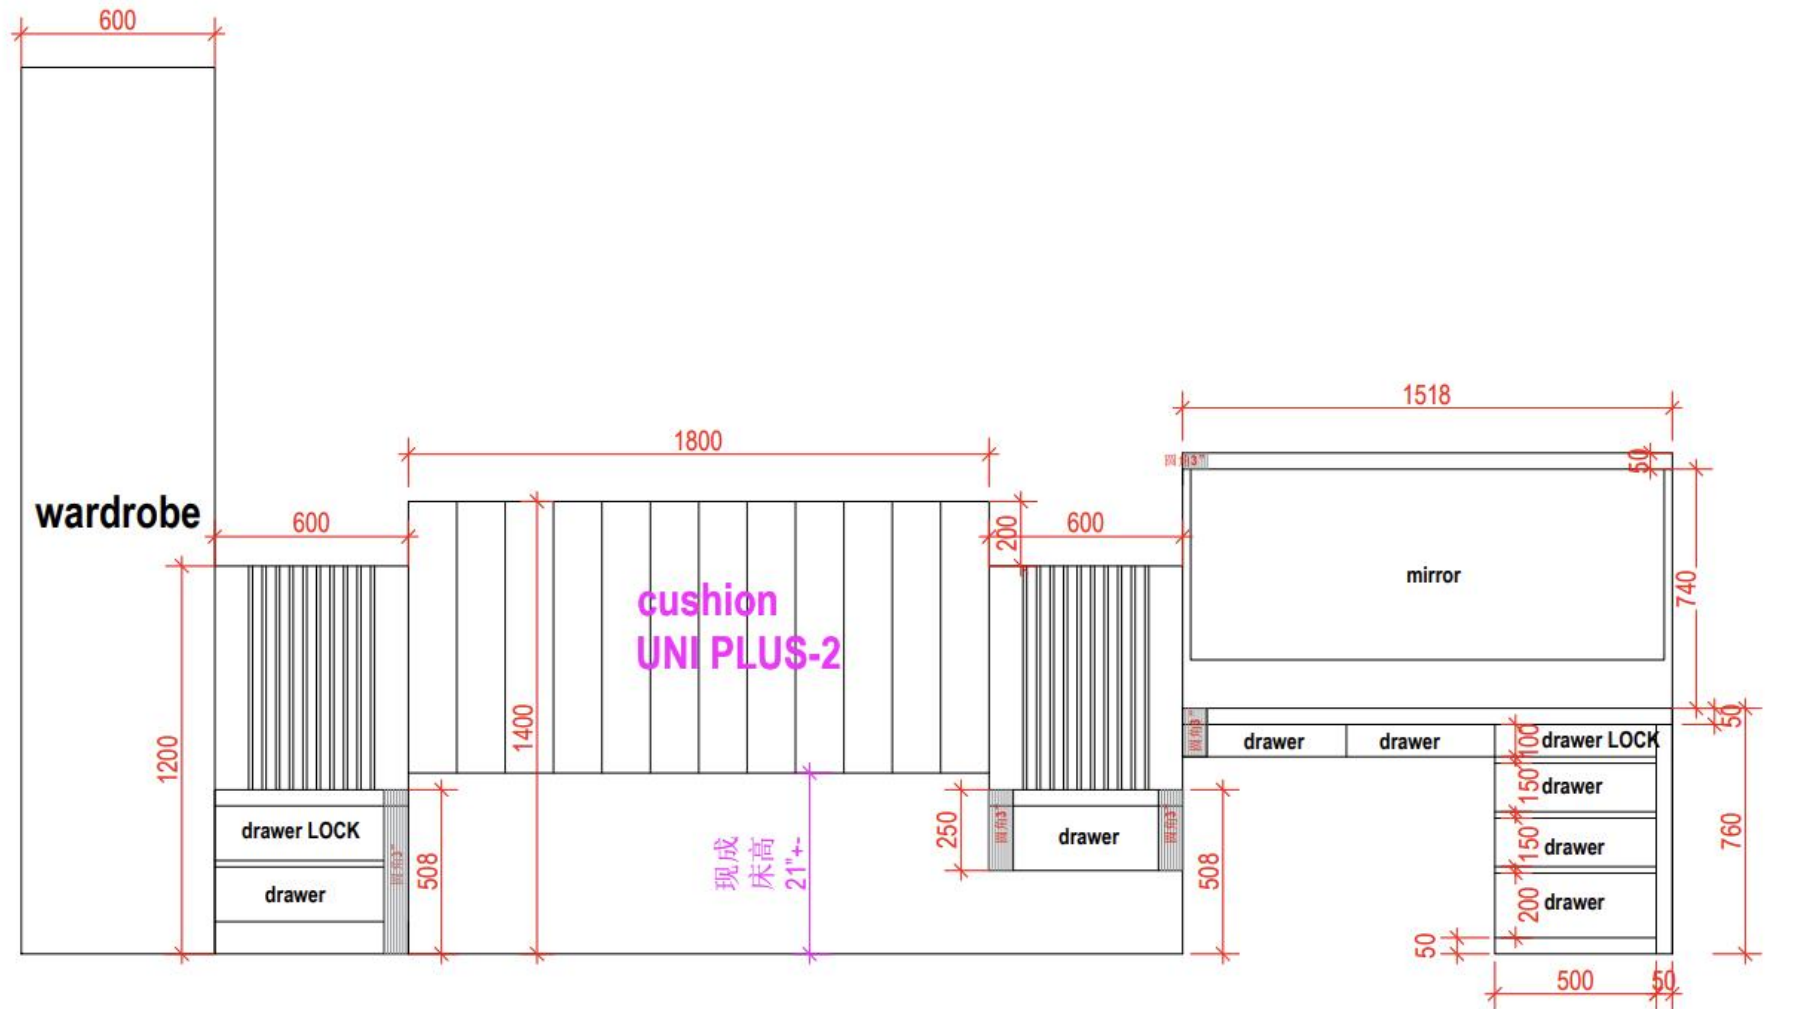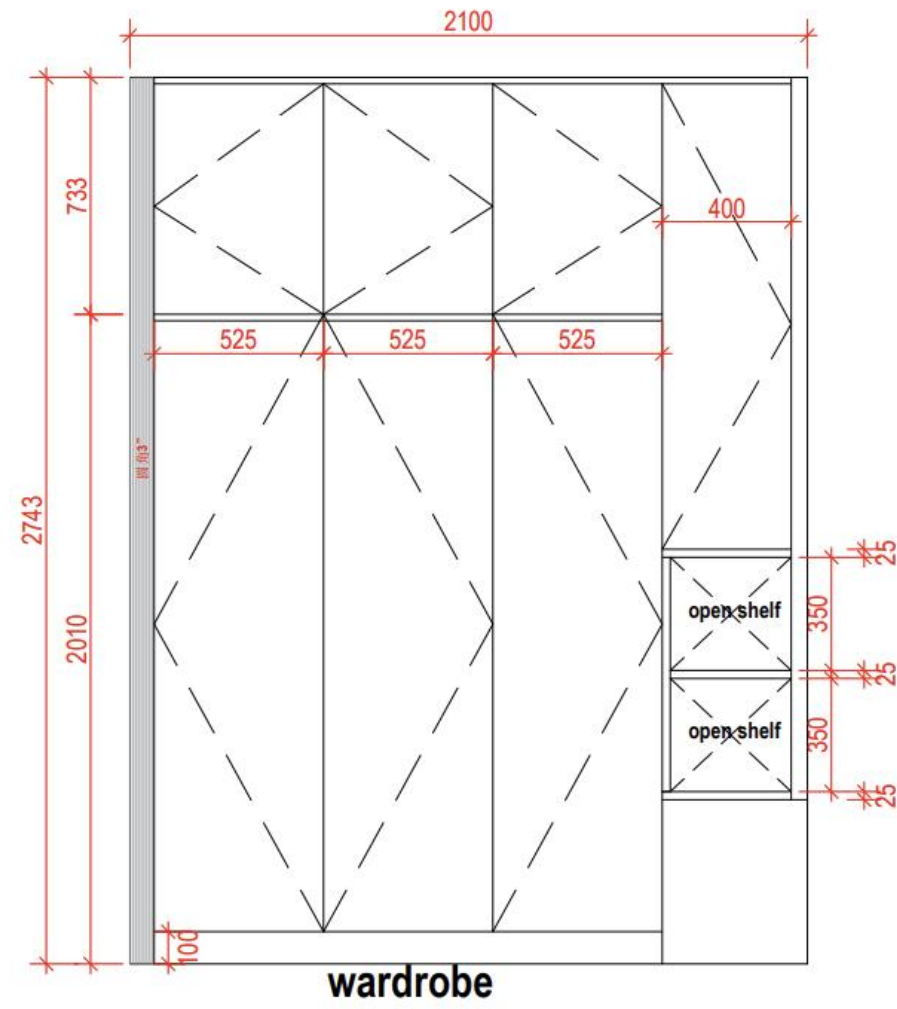


CARPENTRY DRAWING
- DETAILS -

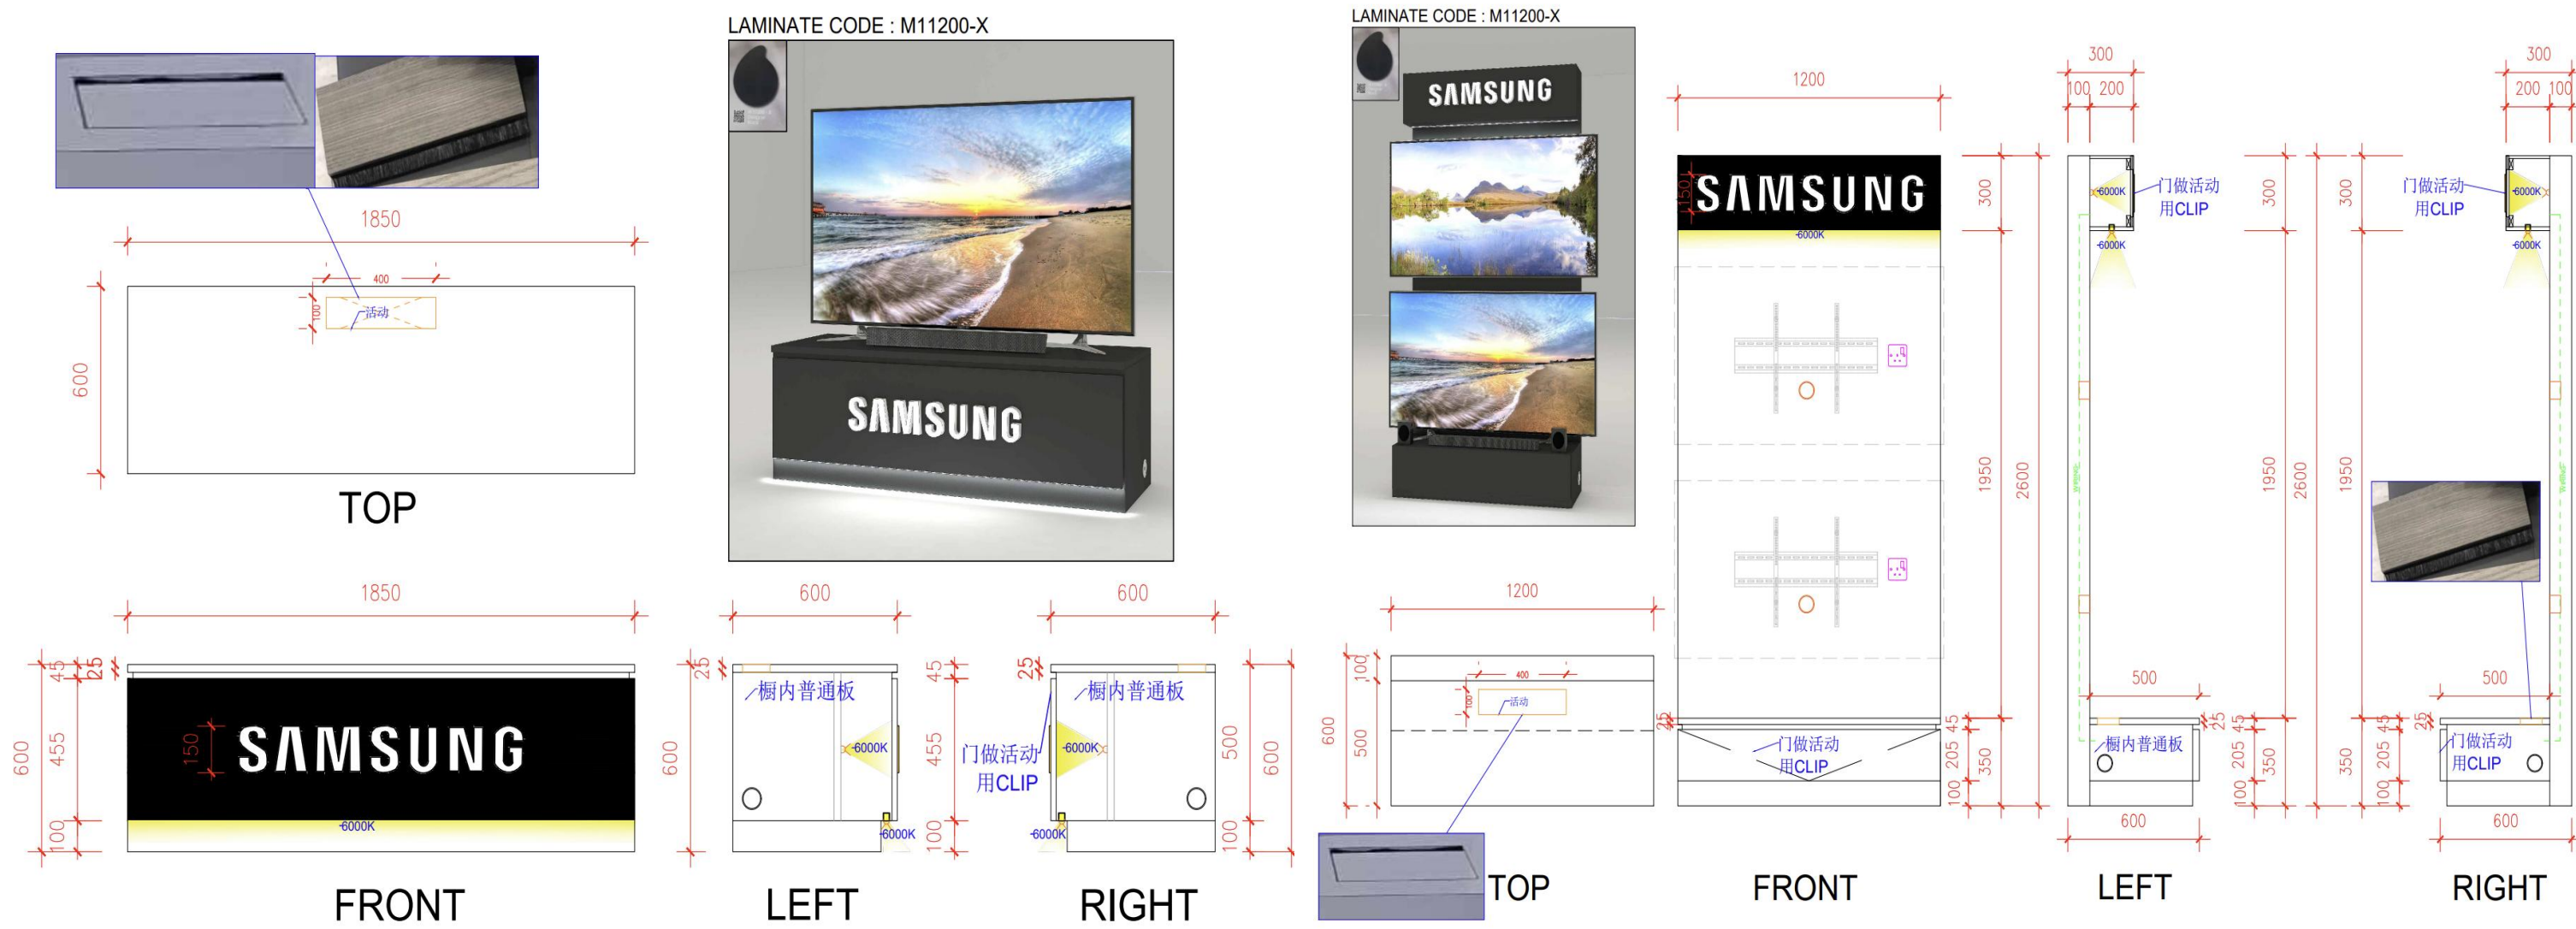

(RESIDENTIAL / COMMERCIAL)




墙砖
CODE: 12201 GLOSSY
H100MM X W200MM

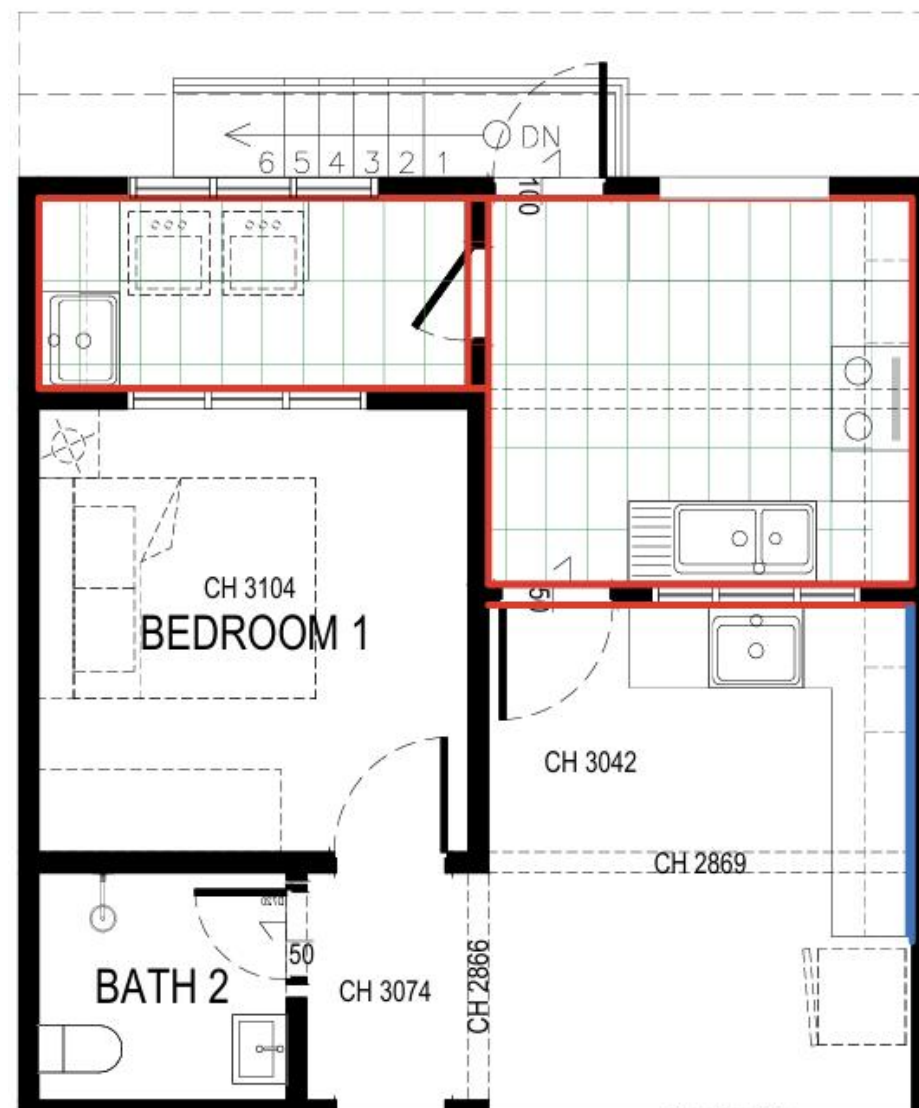

墙砖(湿厨房)
CODE:36000
600MM X 300MM

地砖(湿厨房,洗衣房)
CODE:H63095
600MM X300MM

墙砖 (干厨房)
* 黏工字形
CODE: 12201 GLOSS
H100MM X W200MM

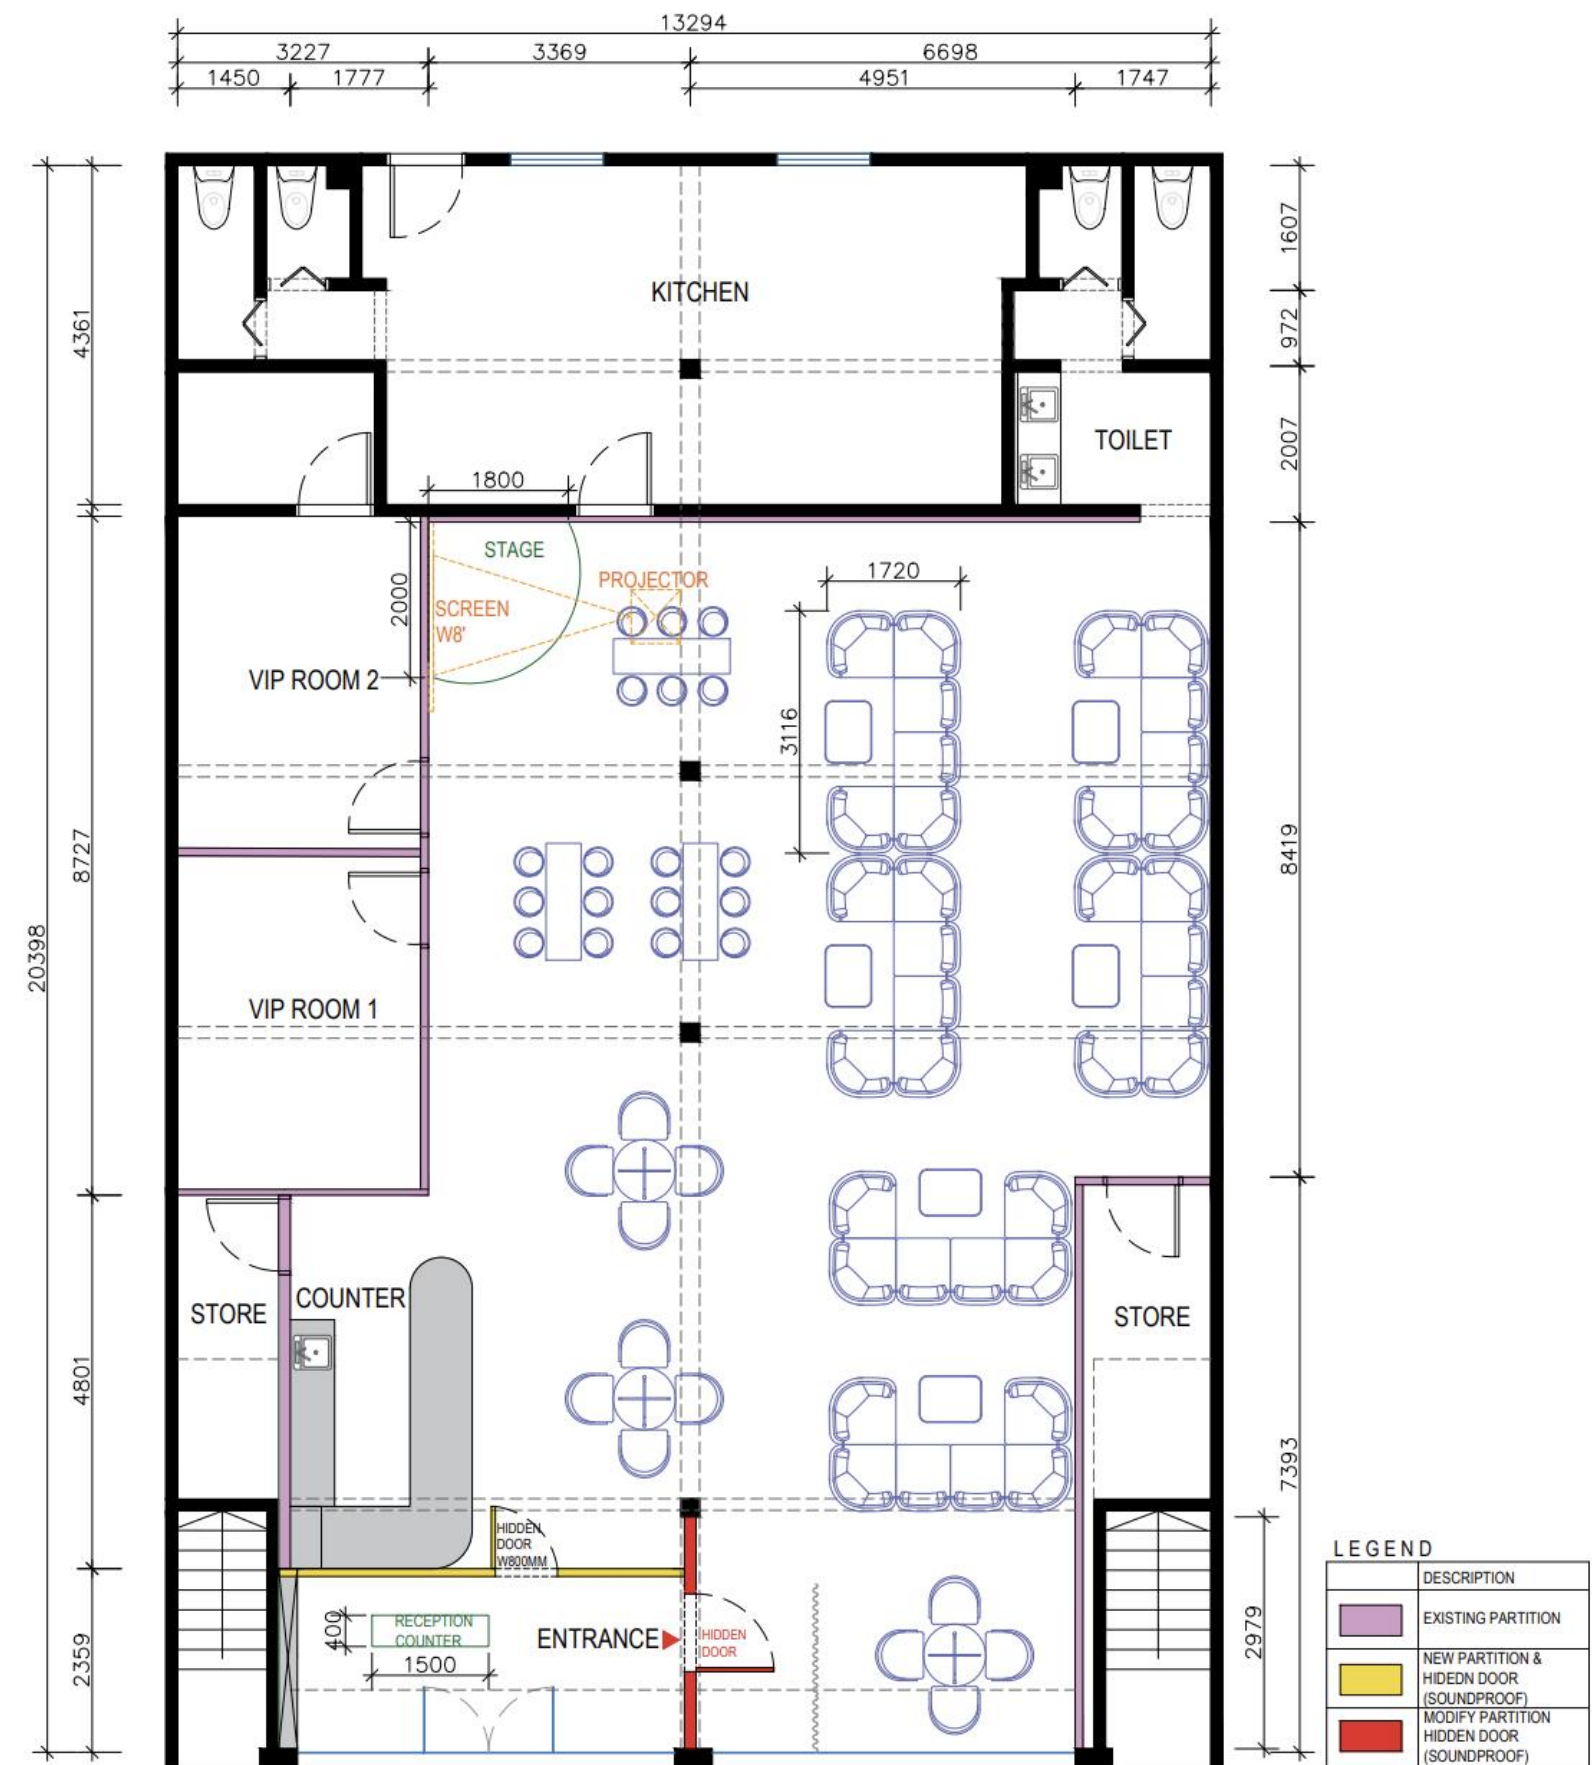

CONSTRUCTION DRAWING (RESIDENTIAL / COMMERCIAL)





L - Floor
Actual Size: 14815 sqft
Display Size: 14385 sqft

ADDITIONAL LIGHT

	HIGH BAY LIGHT (EMART MYDIN) X 15 UNITS
	HIGH BAY LIGHT (NEW) X 3 UNIT
	BACKLIT LED PANEL LIGHT-6000K (NEW) X 12 UNITS



(RESIDENTIAL / COMMERCIAL)

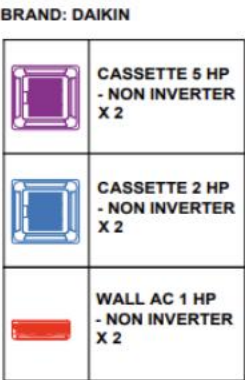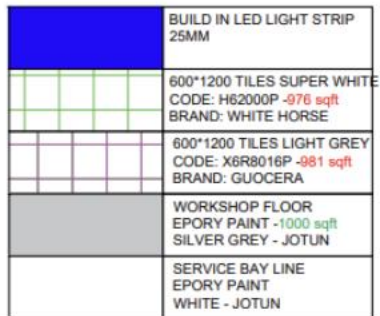



EXTERIOR 3D
(COMMERCIAL PROJECT)



EXTERIOR 3D
(RESIDENTIAL PROJECT)



EXTERIOR 3D
(RESIDENTIAL PROJECT)



INTERIOR 3D
(COMMERCIAL PROJECT – SHOWROOM)




INTERIOR 3D
(COMMERCIAL OFFICE PROJECT)



INTERIOR 3D
(COMMERCIAL OFFICE PROJECT)



INTERIOR 3D
(COMMERCIAL PROJECT – BEAUTY SALON)

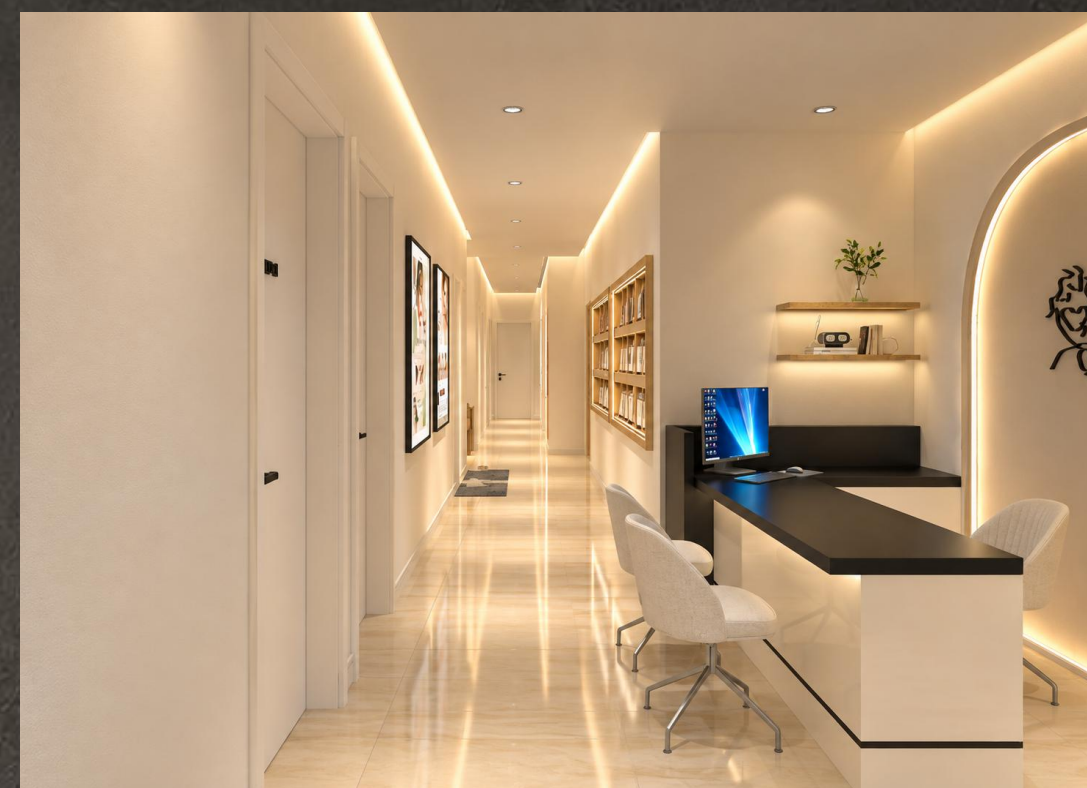


INTERIOR 3D
(COMMERCIAL PROJECT - BEAUTY SALON)



INTERIOR 3D
(COMMERCIAL PROJECT - BEAUTY SALON)



INTERIOR 3D
(RESIDENTIAL PROJECT - LIVING)

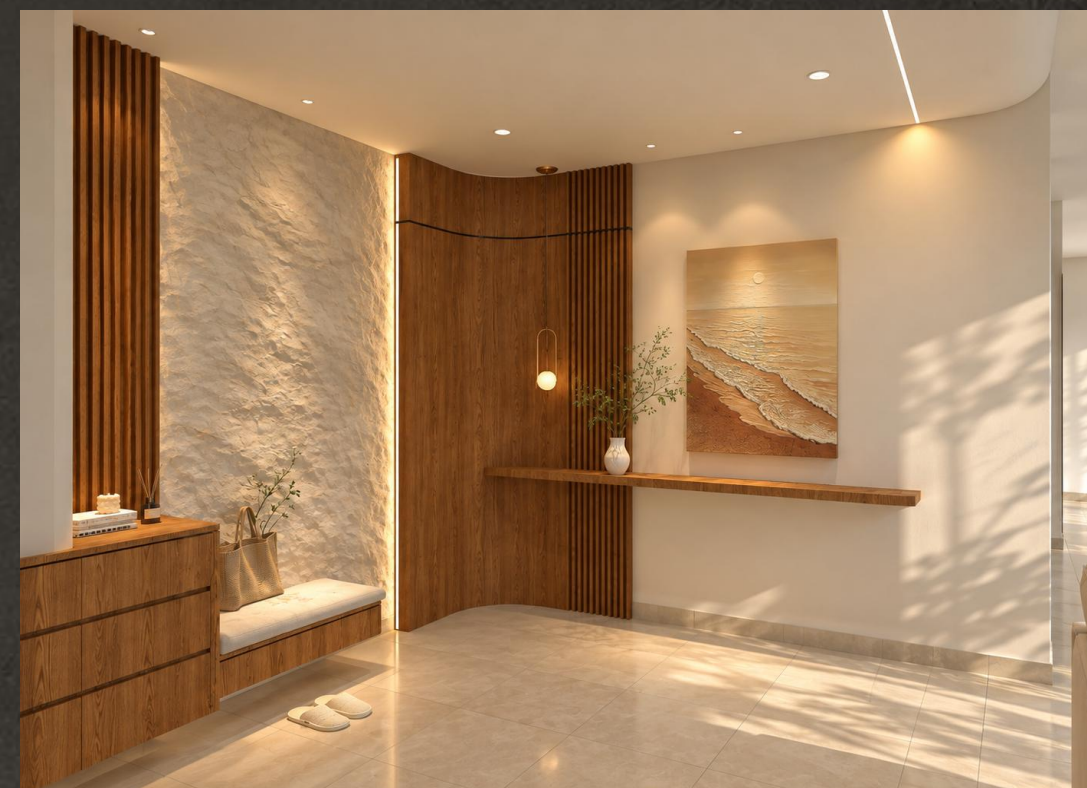

INTERIOR 3D
(RESIDENTIAL PROJECT - LIVING)



INTERIOR 3D
(RESIDENTIAL PROJECT - LIVING)



INTERIOR 3D
(RESIDENTIAL PROJECT – DRY KITCHEN)



INTERIOR 3D
(RESIDENTIAL PROJECT - LIVING)



INTERIOR 3D
(RESIDENTIAL PROJECT – DINING & DRY KITCHEN)



INTERIOR 3D
(RESIDENTIAL PROJECT – DINING & DRY KITCHEN)



INTERIOR 3D
(RESIDENTIAL PROJECT – WET KITCHEN)



INTERIOR 3D
(RESIDENTIAL PROJECT – DRESSING AREA)



INTERIOR 3D
(RESIDENTIAL PROJECT – DINING & KITCHEN)



INTERIOR 3D
(RESIDENTIAL PROJECT – BEDROOM)



INTERIOR 3D
(RESIDENTIAL PROJECT – BEDROOM)



INTERIOR 3D
(RESIDENTIAL PROJECT – BEDROOM)



INTERIOR 3D
(RESIDENTIAL PROJECT – BEDROOM)



INTERIOR 3D
(RESIDENTIAL PROJECT – BEDROOM)



INTERIOR 3D
(COMMERCIAL RETAIL PROJECT)